المملكـــة العربيـــة الســـعودية

رقـم التقـرير ....

التـــاريخ 2026 / 10 /12

المرفقــــات ....

تقـريـر مسـاحـى

لجميع الاغراض

اسم المالك : شركة سمايا الجود

رقم الصـك : ٣٦٠٠٠٢٦٠٣٣٢٩ تـاريخـه : ١٤٤٧/٠٤/٠٧

رقم القطعة : ١٥٣/١٥٢/١ رقم المخطط : ٣٩٦٠

حــــي : ضاحية نمار شـــارع : شارع عرض ٢٠ م

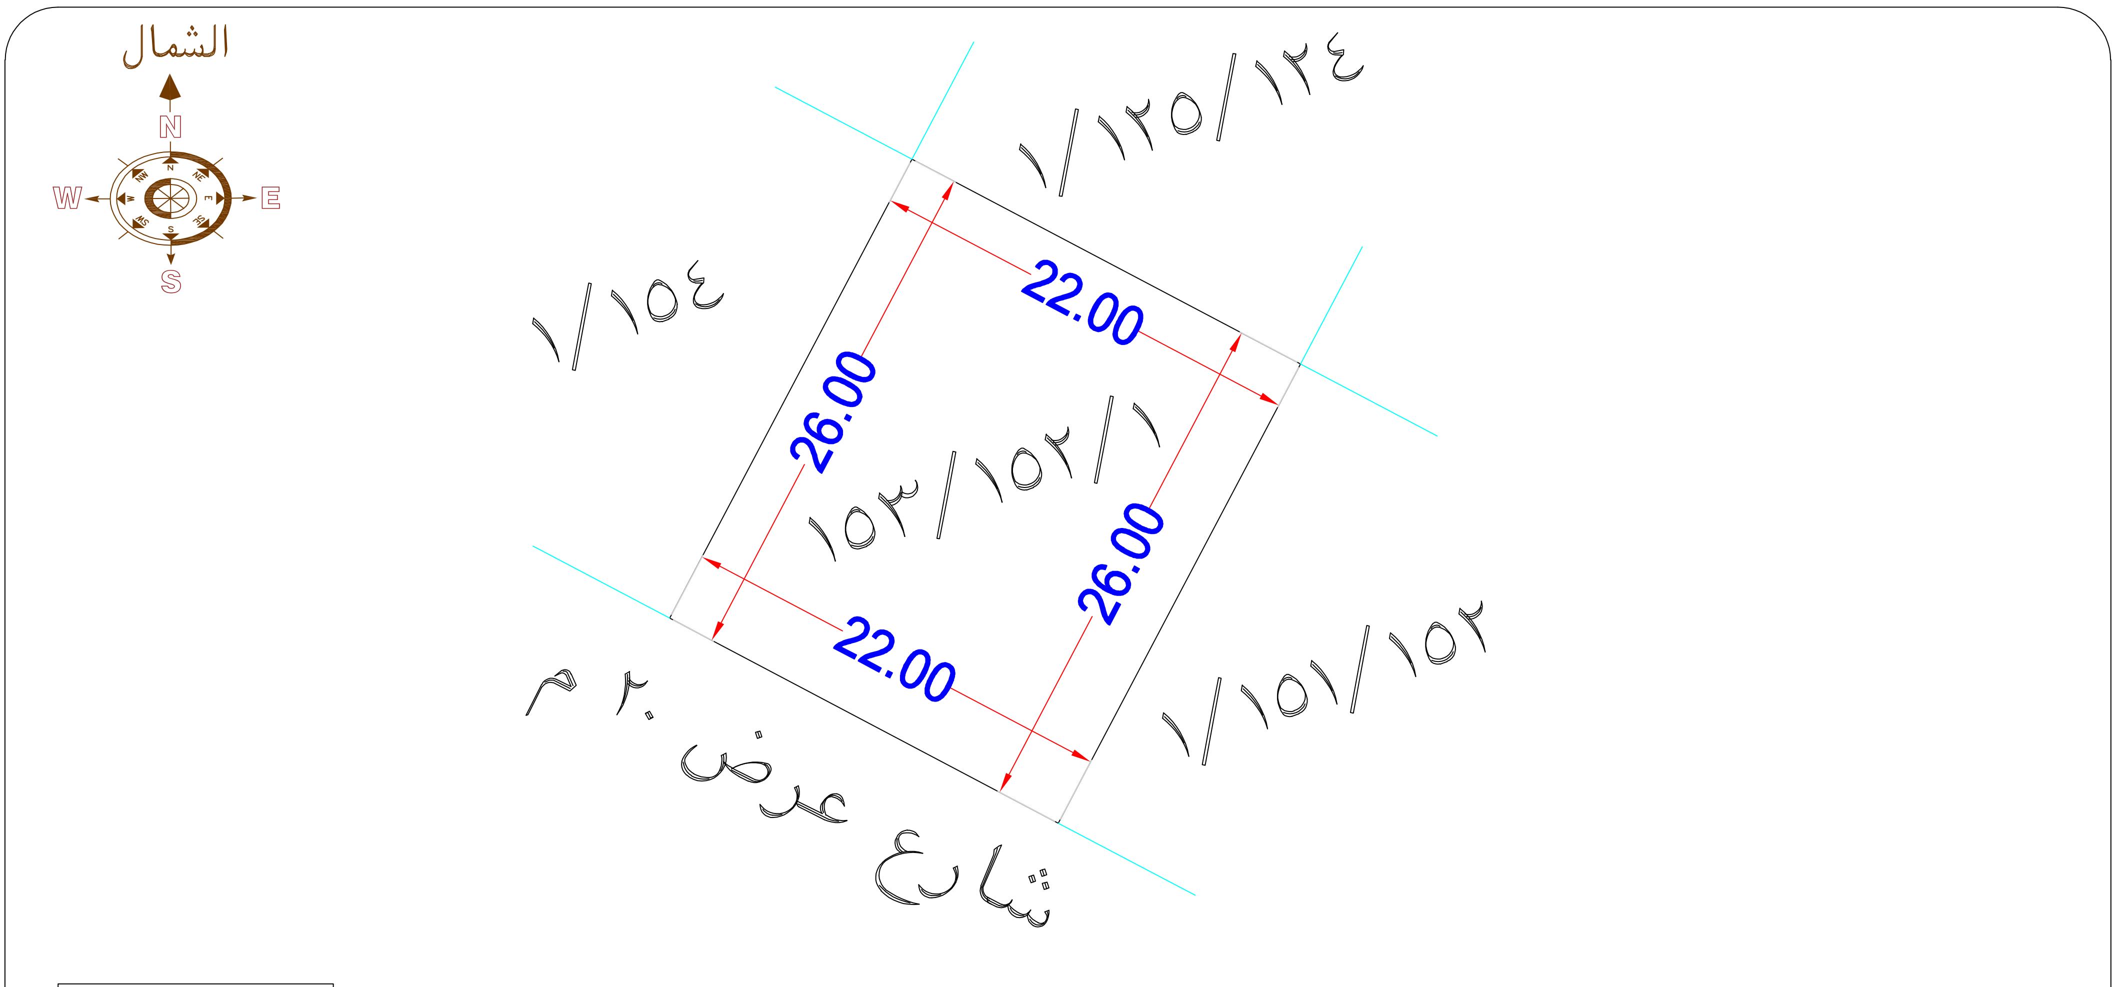

الطريق مسفلت

حـدود وأطـوال ومسـاحـة الـعقـار:

الاتجـاه	الحدود حسب الطبيعة	الطـول	الحدود حسب الصـك	الطـول	الحدود حسب المخطط	الطـول
شمـــال	القطعة رقم ١/١٢٥/١٢٤	٢٢,٠٠	القطعة رقم ١/١٢٥/١٢٤	٢٢,٠٠	القطعة رقم ١/١٢٥/١٢٤	٢٢,٠٠
جنــوب	شارع عرض ٢٠ م	٢٢,٠٠	شارع عرض ٢٠ م	٢٢,٠٠	شارع عرض ٢٠ م	٢٢,٠٠
شـــرق	القطعة رقم ١/١٥١/١٥٢	٢٦,٠٠	القطعة رقم ١/١٥١/١٥٢	٢٦,٠٠	القطعة رقم ١/١٥١/١٥٢	٢٦,٠٠
غـــرب	القطعة رقم ١/١٥٤	٢٦,٠٠	القطعة رقم ١/١٥٤	٢٦,٠٠	القطعة رقم ١/١٥٤	٢٦,٠٠
المساحـة	٥٧٢,٠٠ م ٢		٥٧٢,٠٠ م ٢		٥٧٢,٠٠ م ٢	

ملاحظات : المكتب مسؤول عن صحة الرفع المساحى امام الامانة و الغير

الاسم المهندس راكان الروقى

التوقيع

التاريخ 2026 / 10 /12

أبراج مكة للاستشارات الهندسية
MAKKAH TOWERS ENGINEERING CONSULTANCY